




FACADE LATERALE NORD/OUEST :

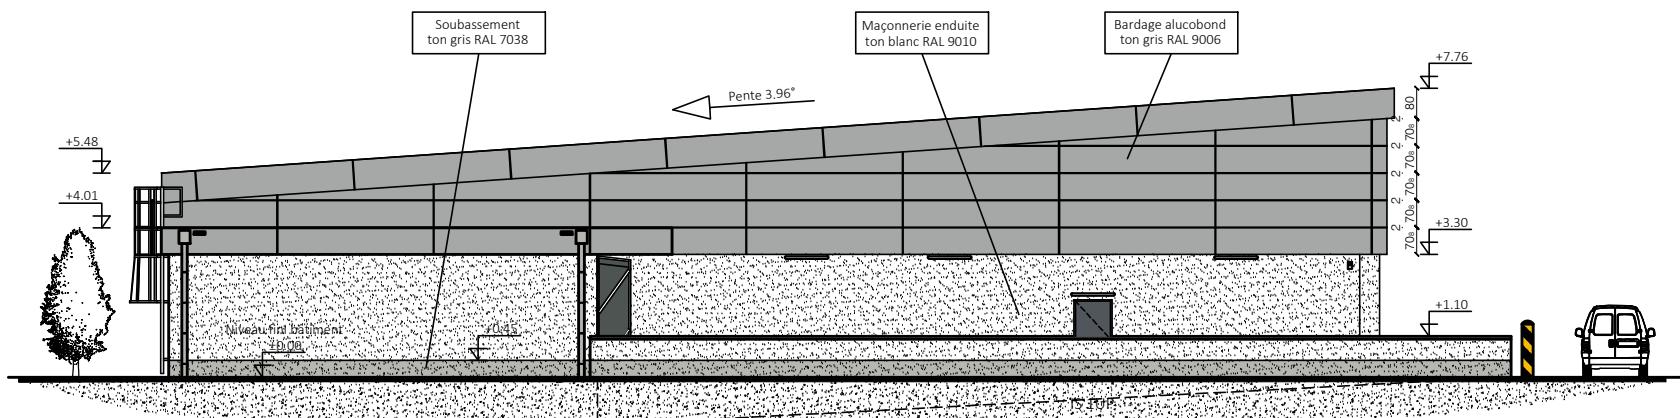

FACADE ARRIERE NORD/EST :

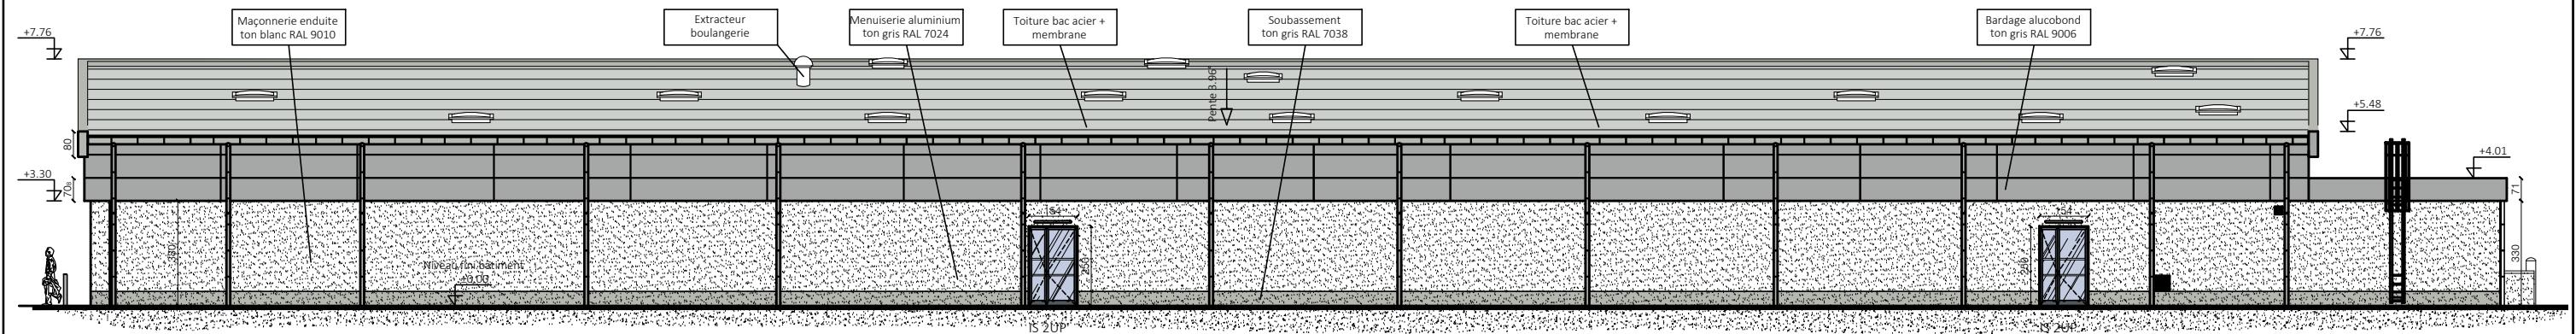

FACADE ARRIERE SUD/EST :

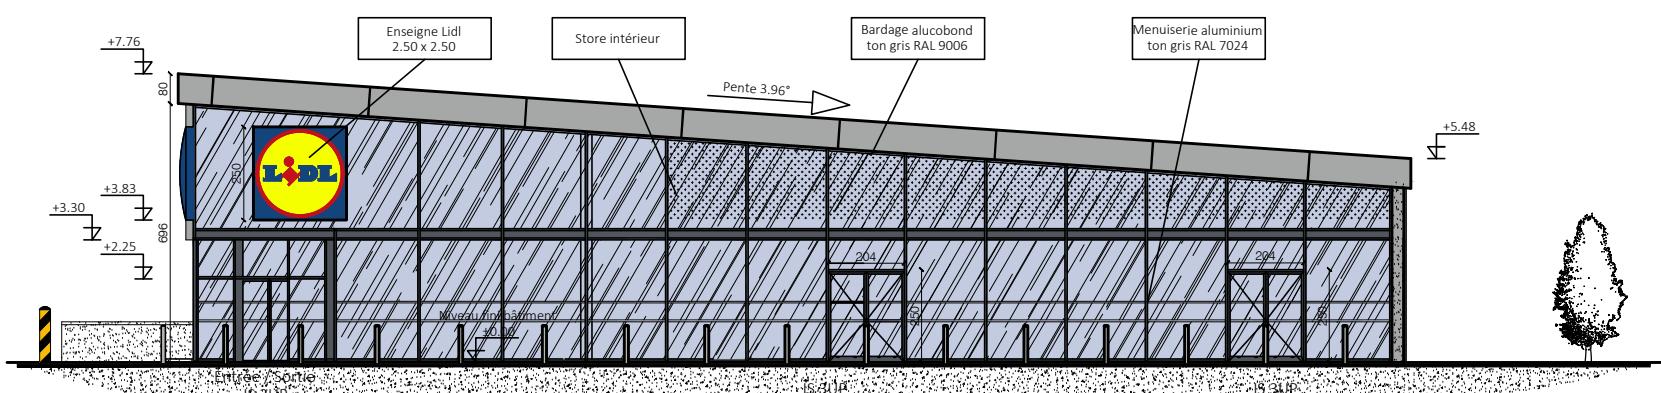

FACADE PRINCIPALE SUD/OUEST :

| Ind. | Date : | Echelle : 1 / 200ème | | Plan Type |
|------|----------|--|--|---------------------------------|
| | | Le 25.02.16 | | |
| 4 | | PLAN DE FACADES PROJETEES | | |
| | | Modifications : | | |
| A | 19.11.15 | Hauteur chéneau et pente toiture | | Magasin Neuf Projet NFK T 14 |
| B | 10.12.15 | Modification trame façade | | |
| C | 18.01.16 | Modification trame ventelles+Stores intérieur+ Sup' épines | | |
| D | 29.01.16 | Modification façade arrière retrait des faux poteaux | | |
| E | 25.02.16 | Retrait véranda | | |

